ANDREA GIAQUINTO

DISEGNATORE CAD E BIM

Portfolio


Dal materiale all’elaborato.


Restituzione tecnica, DWG editabili, modellazione BIM/IFC e rappresentazione degli spazi.


PRECISIONE / LEGGIBILITÀ / METODO

andreagiaquinto.it



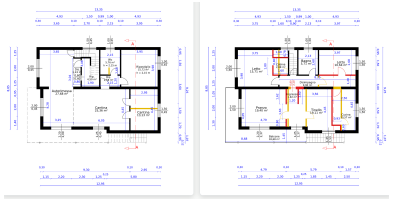

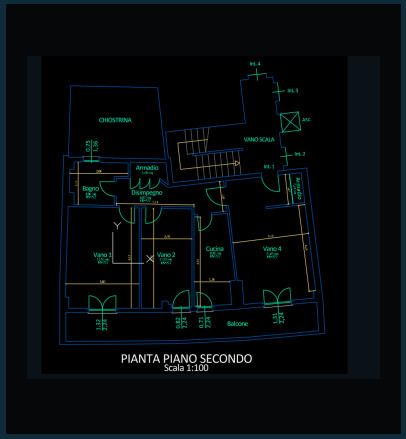

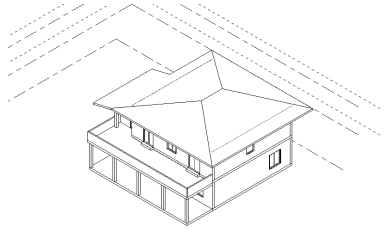

Riproduzione e diffusione vietate senza autorizzazione. andreagiaquinto.it

Un portfolio che continua a crescere.

Qui trovi solo una parte dei lavori svolti per professionisti. Aggiornerò progressivamente il portfolio e il PDF con altri elaborati: ho molti progetti, appartenenti a diverse tipologie di lavorazione, ancora da presentare.

RICHIESTE REALI

Gli elaborati sono stati sviluppati su incarichi reali, secondo le richieste, i materiali e le specifiche dei professionisti committenti.

STANDARD PERSONALIZZABILI

Non sono modelli standard da riprodurre. Geometrie, layer, stili, contenuti e impaginazione vengono adattati alle esigenze di ogni nuovo incarico.

USO DEL PORTFOLIO

Immagini e tavole sono presentate per documentare il lavoro svolto. Le riproduzioni sono fuori scala e non sostituiscono gli elaborati originali.

TUTELA DEI CONTENUTI

È vietata la copia, la riproduzione, la ripubblicazione su altri siti e la diffusione, anche parziale, dei contenuti senza autorizzazione scritta. Il PDF è scaricabile per consultazione personale e per valutare una collaborazione.


Layer, colori, stili di testo e quota, cartigli e altri standard grafici possono derivare dal professionista o dal file sorgente. Sono indicativi e adattabili allo standard richiesto.


Riproduzione e diffusione vietate senza autorizzazione. andreagiaquinto.it

SELEZIONE DI ELABORATI

Tre percorsi, un metodo comune.

Leggere il materiale di partenza. Organizzare le informazioni. Restituire elaborati utili al lavoro tecnico e alla presentazione.

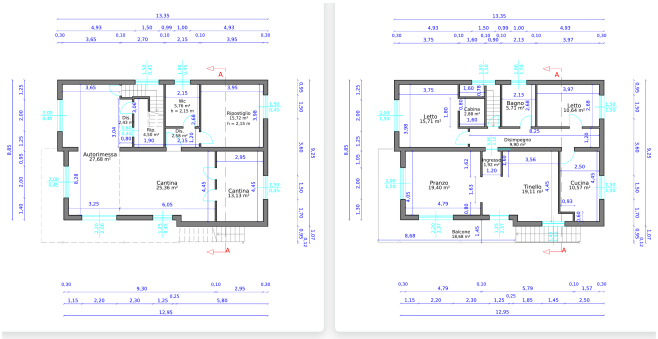

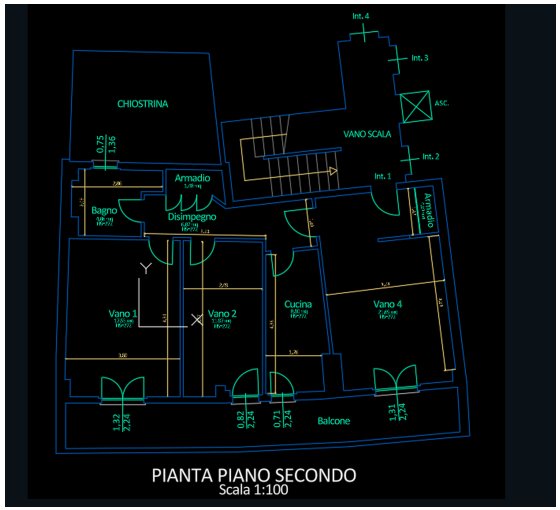



A / DAI DOCUMENTI AL CAD/BIM

DWG e schizzi, scansioni, viste renderizzate e modello IFC: tre percorsi di restituzione.

Da pagina 04

B / DALLA NUVOLA AL CAD

La sezione del rilievo e la planimetria ottenuta, con lettura e controllo delle geometrie.

Da pagina 14

C / PLANIMETRIE COMMERCIALI

Due casi residenziali, rappresentati in pianta arredata e in vista tridimensionale.

Da pagina 17

Riproduzioni di presentazione, fuori scala. Per misure e contenuti tecnici fanno fede gli elaborati originali.

Layer, colori, stili di testo e quota, cartigli e altri standard grafici possono derivare dal professionista o dal file sorgente. Sono indicativi e adattabili allo standard richiesto.

Riproduzione e diffusione vietate senza autorizzazione. andreagiaquinto.it

A


Dai documenti al CAD e al BIM

Schizzi, file esistenti, PDF e scansioni diventano disegni modificabili, tavole coordinate e modelli di interscambio.

01 DWG + schizzo / progetto e comparativo

02 Scansione / planimetria DWG

03 Tavola PDF / viste 3D e IFC

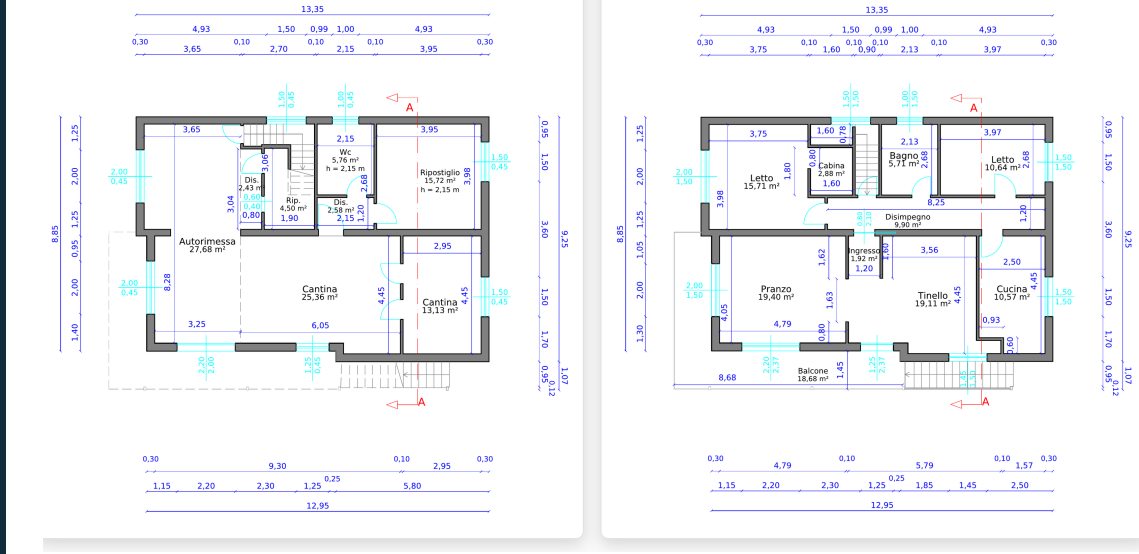

Riproduzione e diffusione vietate senza autorizzazione. andreagiaquinto.it

Prima, leggere e confrontare.


La base CAD definisce il riferimento geometrico; gli schizzi descrivono le modifiche distributive richieste.

BASE CAD RICEVUTA




Andrea Giaquinto | Disegnatore CAD/BIM | andreagiaquinto.it

SCHIZZI DEL COMMITTENTE

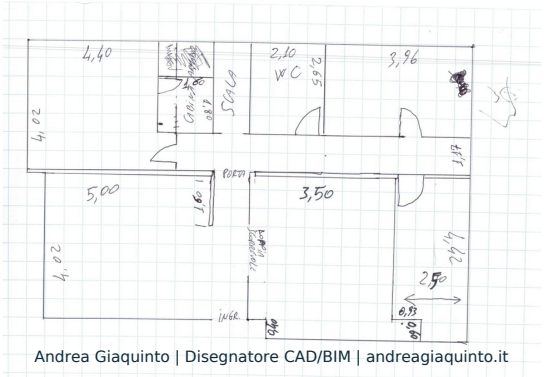

Andrea Giaquinto | Disegnatore CAD/BIM | andreagiaquinto.it

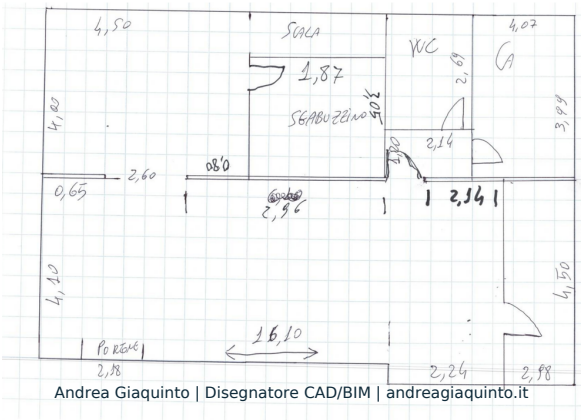

Andrea Giaquinto | Disegnatore CAD/BIM | andreagiaquinto.it


Base metrica e modifiche vengono confrontate prima di organizzare le tavole finali.

Layer, colori, stili di testo e quota, cartigli e altri standard grafici possono derivare dal professionista o dal file sorgente. Sono indicativi e adattabili allo standard richiesto.

Riproduzione e diffusione vietate senza autorizzazione. andreagiaquinto.it

Lo stato di fatto, coordinato.

Piante dei due livelli organizzate per confrontare geometrie, aperture, collegamenti e quote.

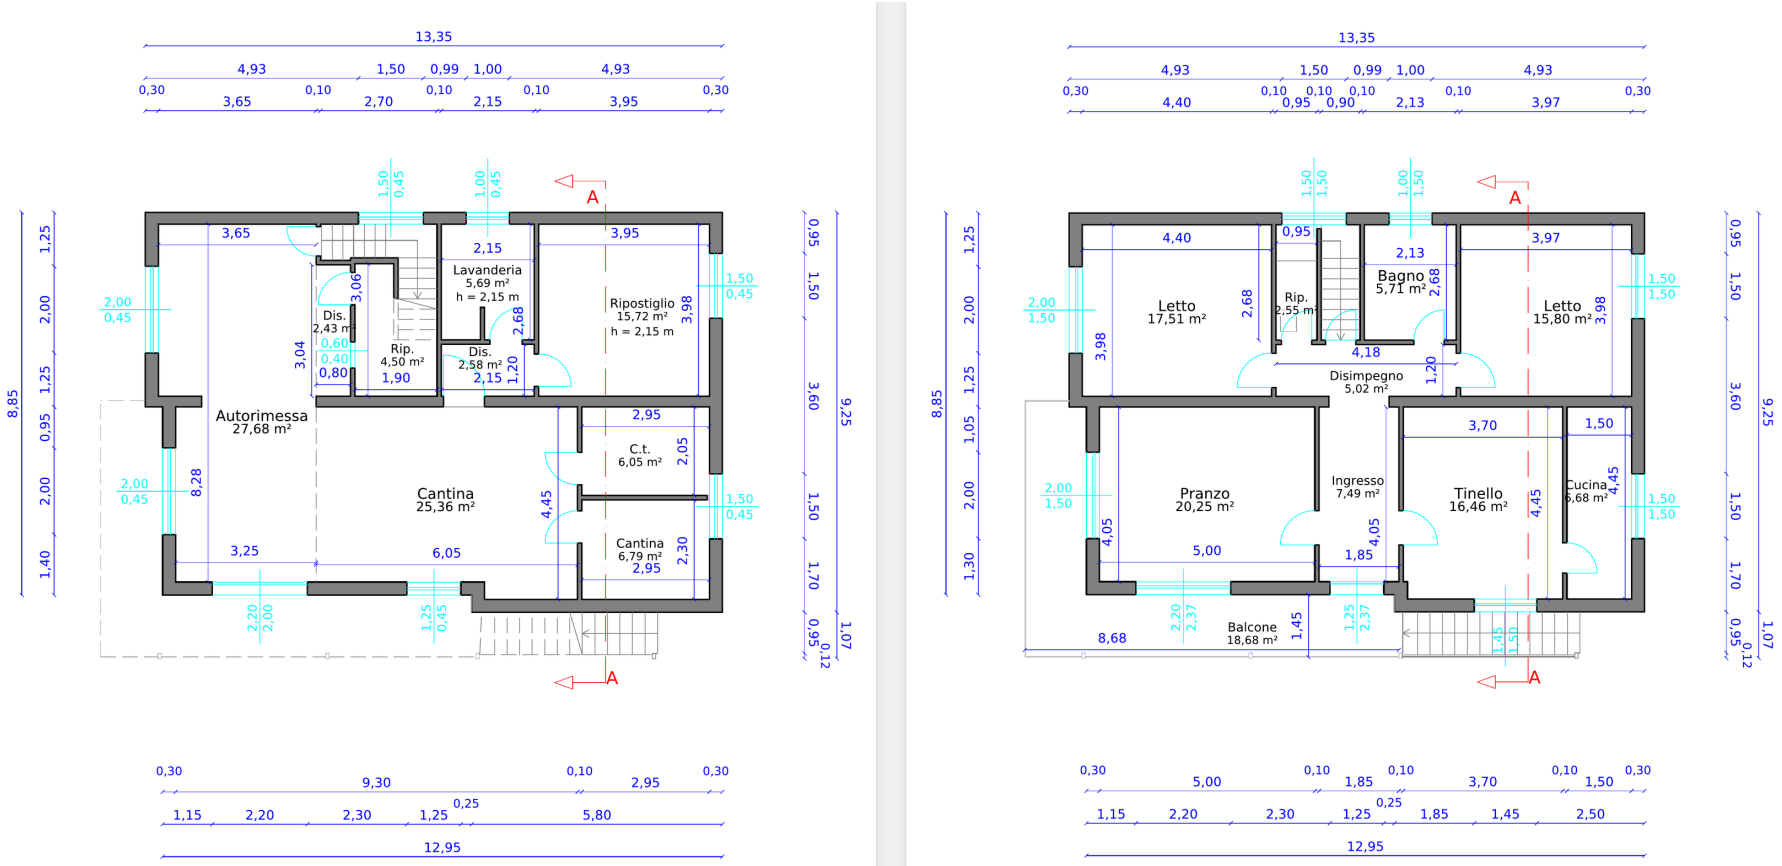

Andrea Giaquinto | Disegnatore CAD/BIM | andreagiaquinto.it


DWG EDITABILE / TAVOLE COORDINATE

Layer, colori, stili di testo e quota, cartigli e altri standard grafici possono derivare dal professionista o dal file sorgente. Sono indicativi e adattabili allo standard richiesto.

Riproduzione e diffusione vietate senza autorizzazione. andreagiaquinto.it

Le modifiche diventano disegno.

La nuova distribuzione viene restituita in tavole CAD coordinate, mantenendo leggibile il rapporto con la base esistente.

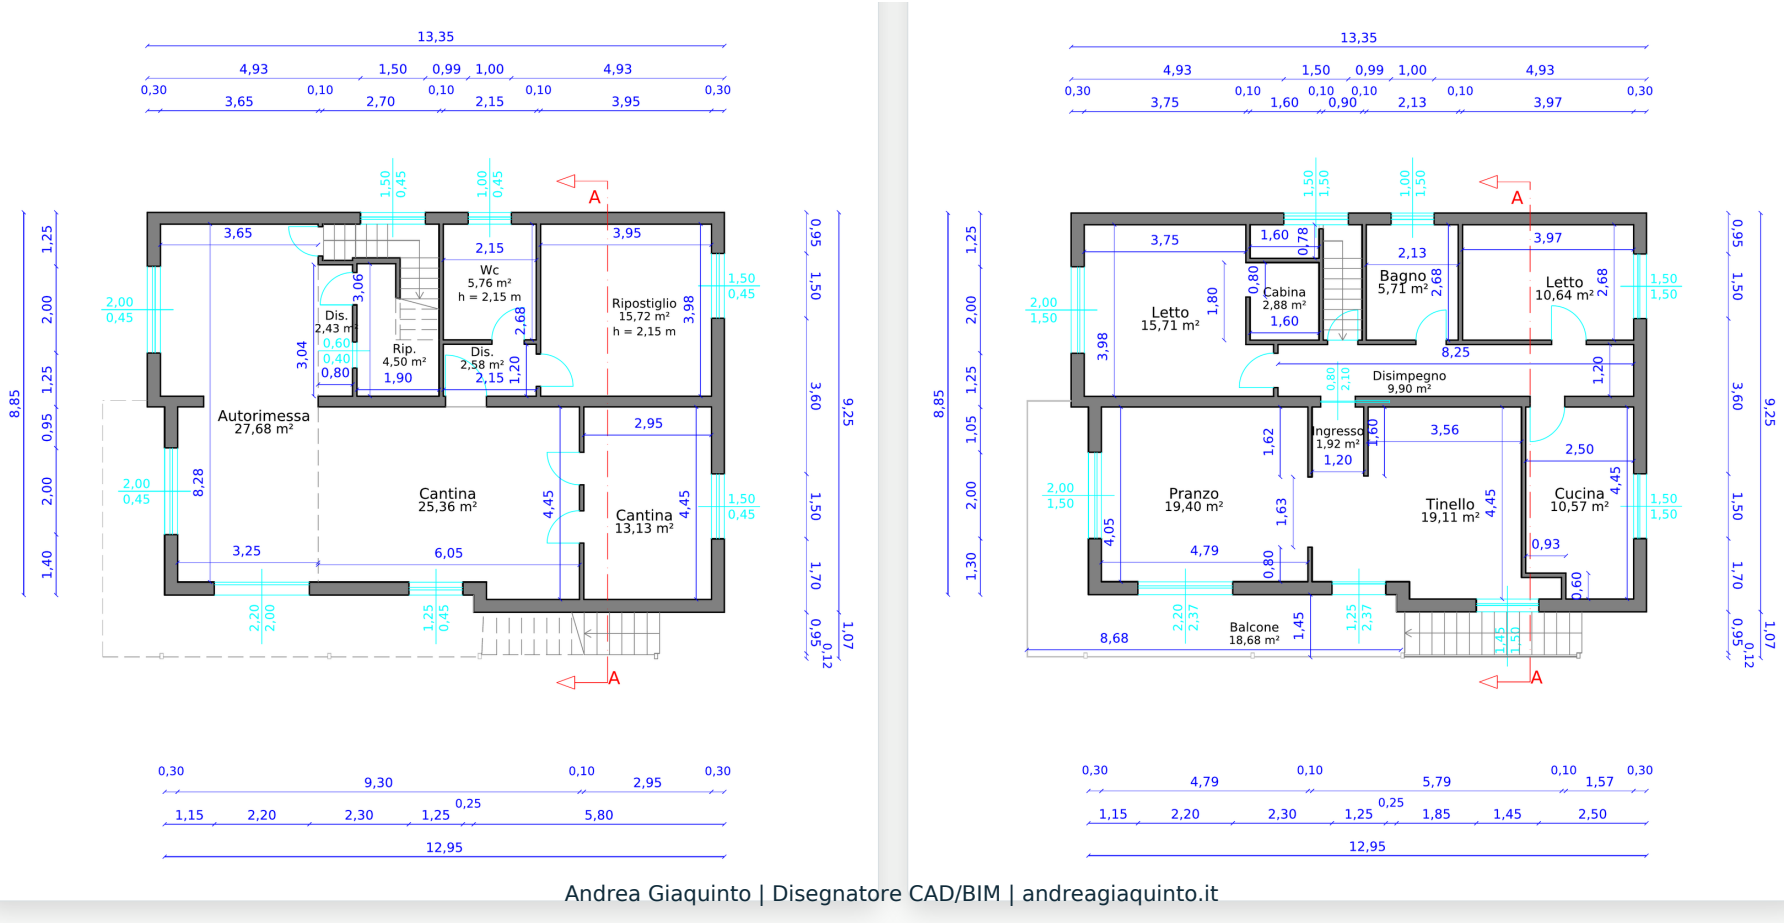

Andrea Giaquinto | Disegnatore CAD/BIM | andreagiaquinto.it


DWG EDITABILE / TAVOLE COORDINATE

Layer, colori, stili di testo e quota, cartigli e altri standard grafici possono derivare dal professionista o dal file sorgente. Sono indicativi e adattabili allo standard richiesto.

Riproduzione e diffusione vietate senza autorizzazione. andreagiaquinto.it

Un confronto che si legge.

Demolizioni e costruzioni vengono rappresentate in una tavola comparativa, separando gli interventi dalle parti mantenute.

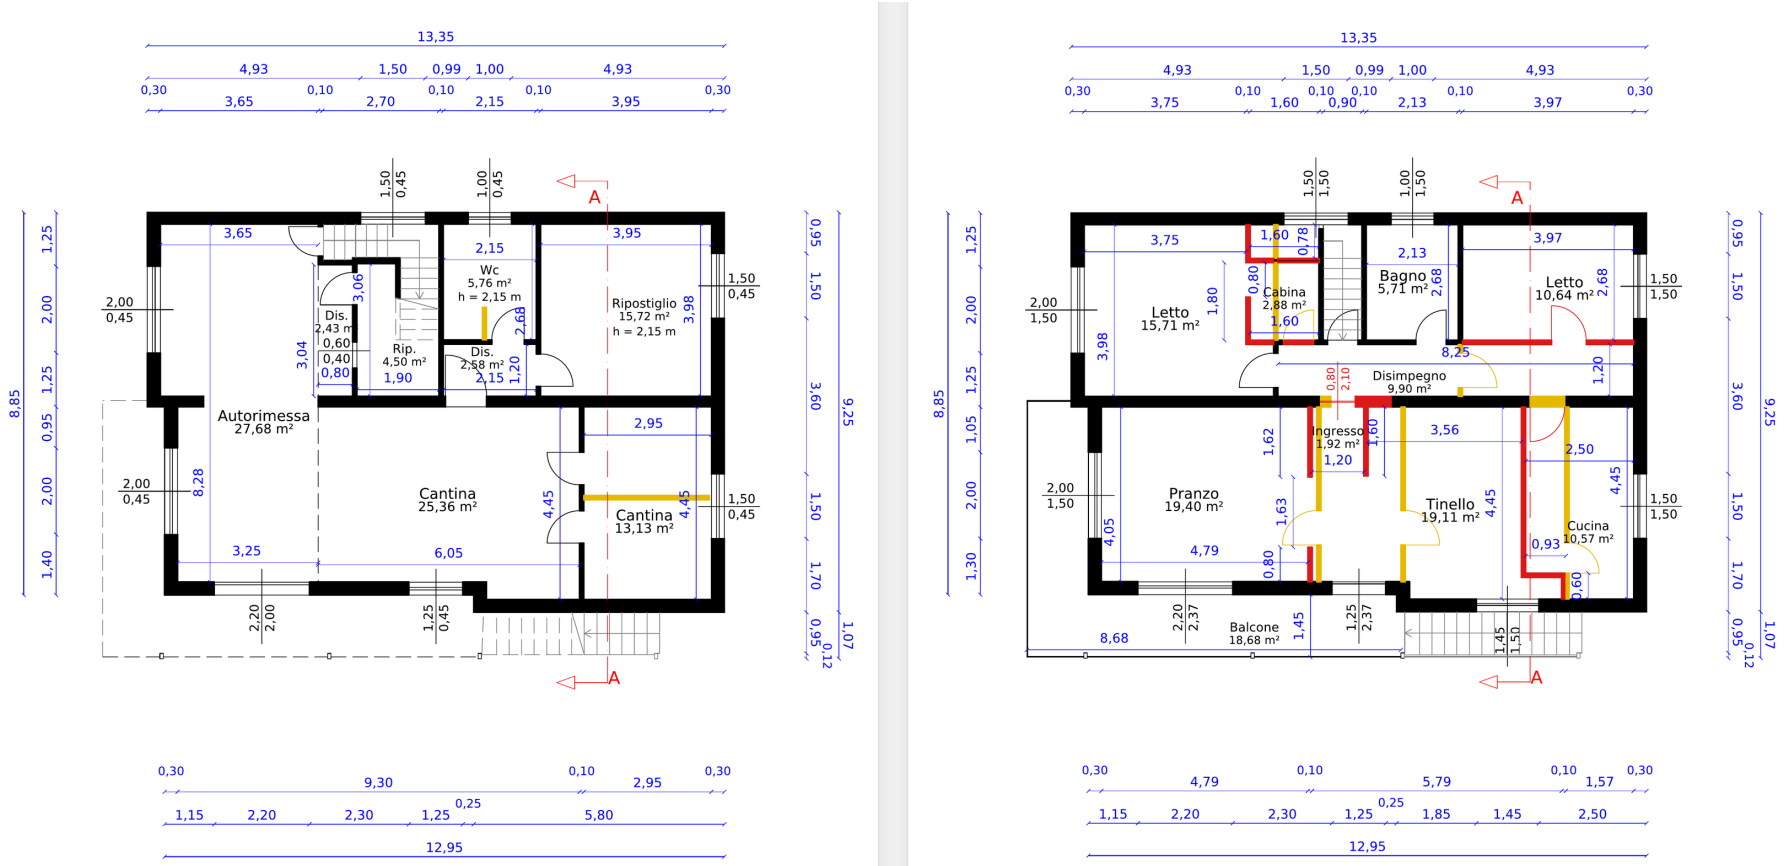

Andrea Giaquinto | Disegnatore CAD/BIM | andreagiaquinto.it

Demolizioni

Costruzioni

Colori secondo la convenzione del file sorgente.


Layer, colori, stili di testo e quota, cartigli e altri standard grafici possono derivare dal professionista o dal file sorgente. Sono indicativi e adattabili allo standard richiesto.

Riproduzione e diffusione vietate senza autorizzazione. andreagiaquinto.it


Dalla carta alla geometria.

Dettagli dei documenti ricevuti: una base scansionata e le annotazioni con misure e indicazioni di rilievo.

DETTAGLIO DELLA SCANSIONE

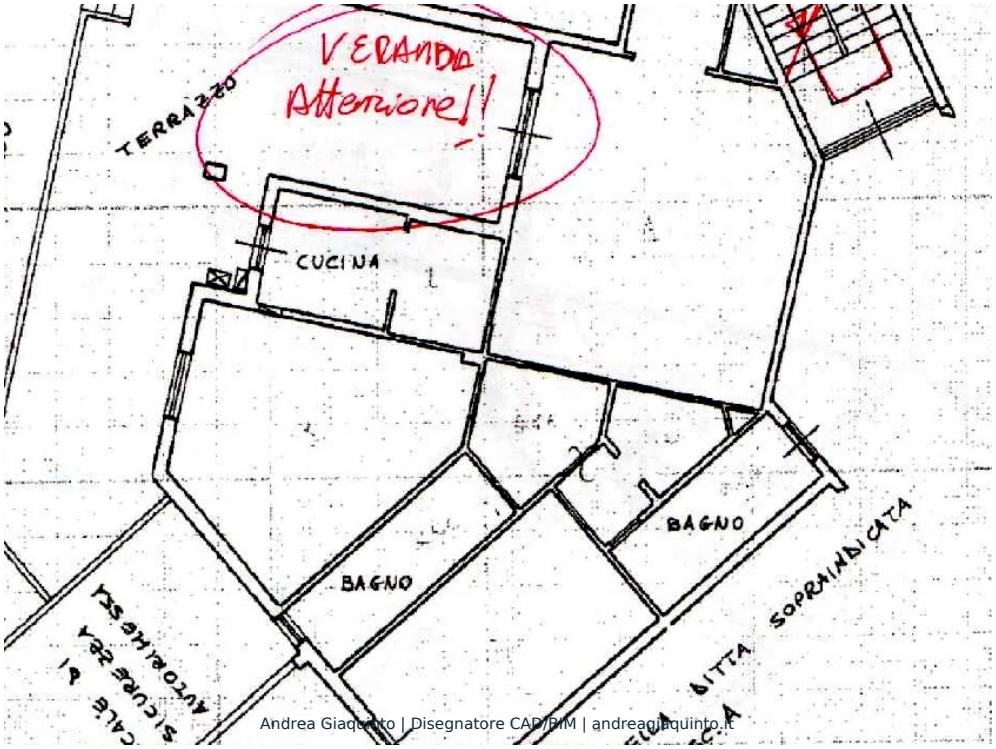

DETTAGLIO CON MISURE E ANNOTAZIONI

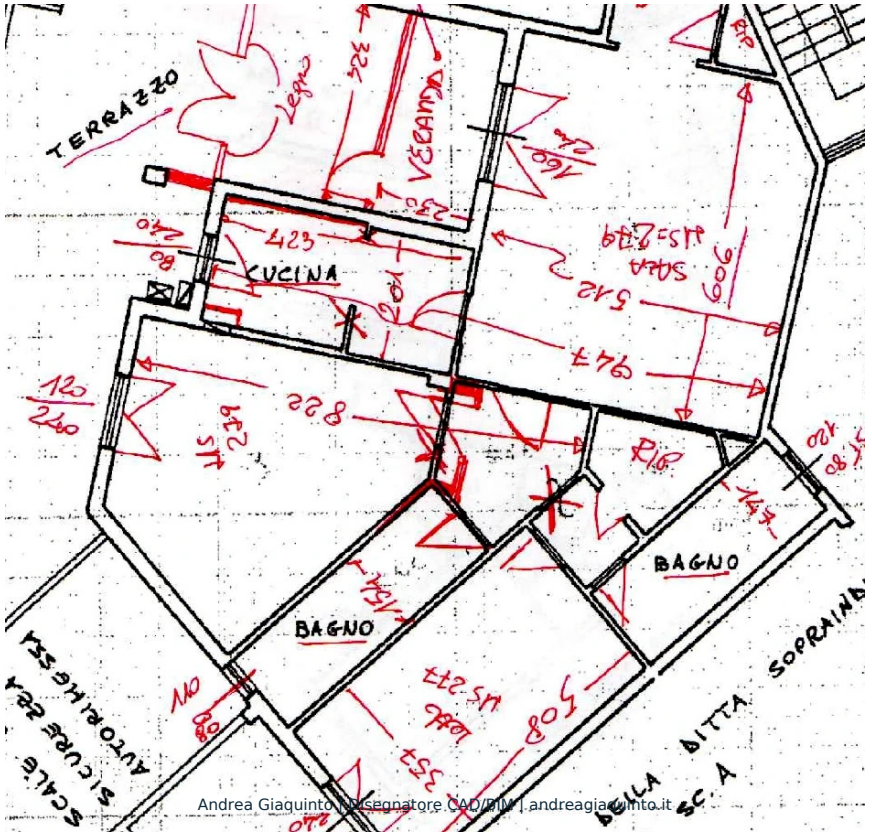


I margini identificativi sono esclusi dalla presentazione. Le annotazioni tecniche vengono interpretate e confrontate con la base disponibile.

Layer, colori, stili di testo e quota, cartigli e altri standard grafici possono derivare dal professionista o dal file sorgente. Sono indicativi e adattabili allo standard richiesto.

Riproduzione e diffusione vietate senza autorizzazione. andreagiaquinto.it

Un DWG che si può aggiornare.

Geometria vettoriale, ambienti, aperture e quote organizzati in un elaborato modificabile.

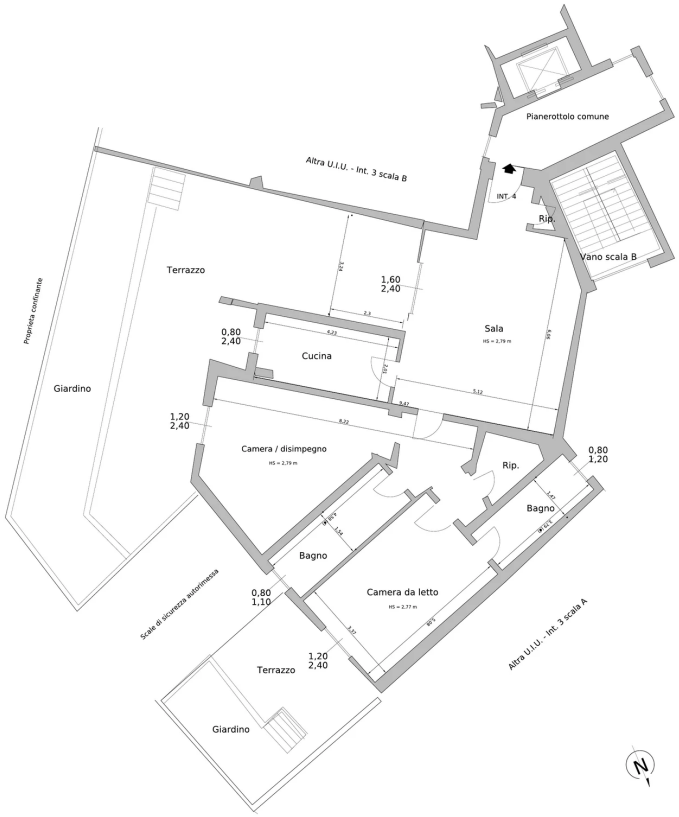

PIANTA PIANO TERRA
Scala 1:100


Andrea Giaquinto | Disegnatore CAD/BIM | andreagiaquinto.it

RESTITUZIONE CAD

Ricostruzione della planimetria e lettura coordinata di muri, aperture e spazi accessori.

UTILIZZO DEL FILE

Aggiornamento del disegno, impaginazione delle tavole e adeguamento agli standard del professionista.

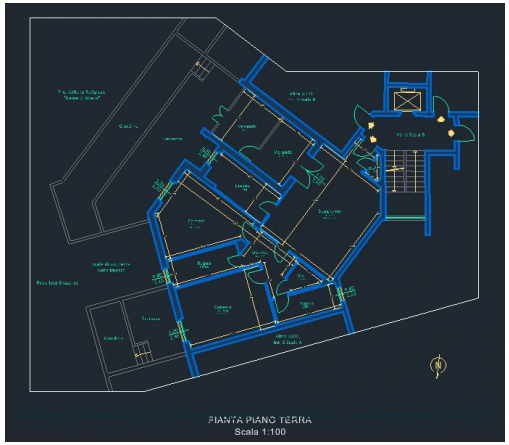


Layer, colori, stili di testo e quota, cartigli e altri standard grafici possono derivare dal professionista o dal file sorgente. Sono indicativi e adattabili allo standard richiesto.

Riproduzione e diffusione vietate senza autorizzazione. andreagiaquinto.it

Leggere l’edificio nel suo insieme.


Piante, copertura, prospetti e sezioni vengono messi in relazione prima della ricostruzione tridimensionale.

PROSPETTI E SEZIONE

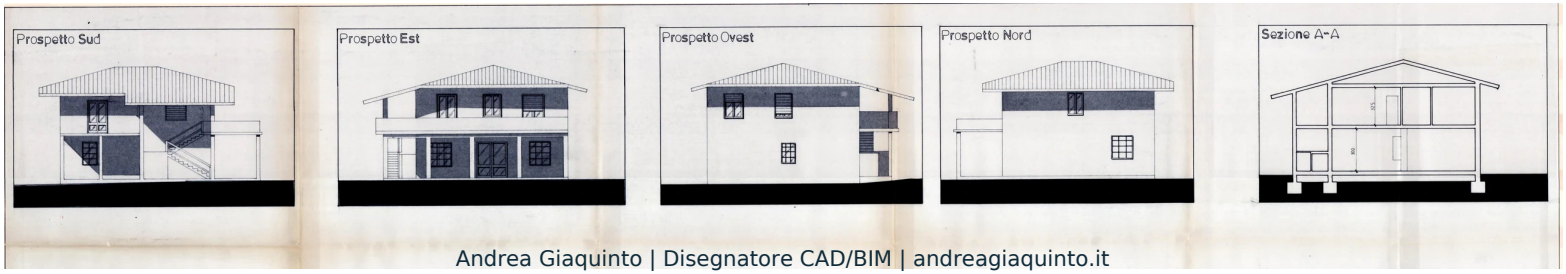


Andrea Giaquinto | Disegnatore CAD/BIM | andreagiaquinto.it

PIANTE E COPERTURA

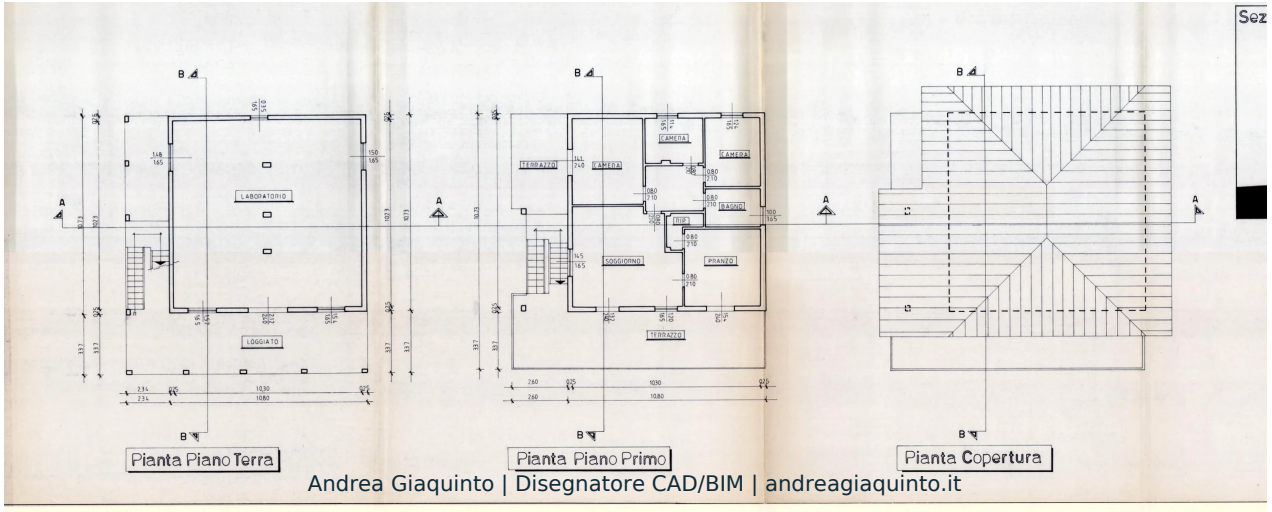

Andrea Giaquinto | Disegnatore CAD/BIM | andreagiaquinto.it

SEZIONI

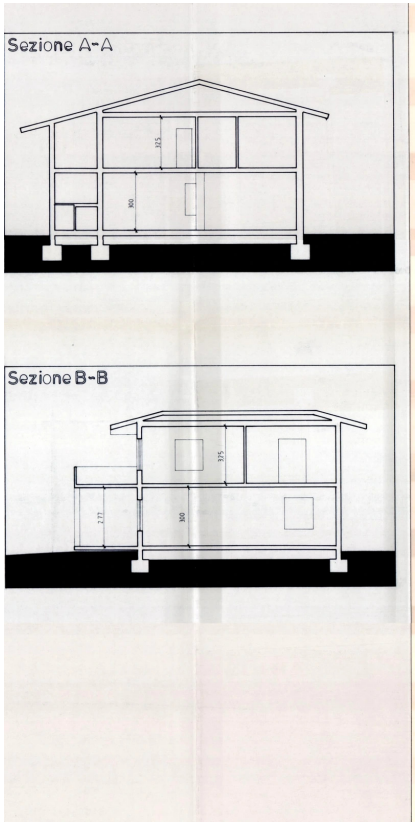

Andrea Giaquinto | Disegnatore CAD/BIM | andreagiaquinto.it

Layer, colori, stili di testo e quota, cartigli e altri standard grafici possono derivare dal professionista o dal file sorgente. Sono indicativi e adattabili allo standard richiesto.

Riproduzione e diffusione vietate senza autorizzazione. andreagiaquinto.it

Volumi, facciate, relazioni.

Viste del modello e sezioni tridimensionali per comunicare l’organizzazione dell’edificio.



Andrea Giaquinto | Disegnatore CAD/BIM | andreagiaquinto.it



Andrea Giaquinto | Disegnatore CAD/BIM | andreagiaquinto.it

VISTA ALTERNATIVA



Andrea Giaquinto | Disegnatore CAD/BIM | andreagiaquinto.it


SEZIONI TRIDIMENSIONALI

Layer, colori, stili di testo e quota, cartigli e altri standard grafici possono derivare dal professionista o dal file sorgente. Sono indicativi e adattabili allo standard richiesto.

Riproduzione e diffusione vietate senza autorizzazione. andreagiaquinto.it

Un modello aperto all’interscambio.

Vista del modello IFC importato in Revit, con una lettura chiara di copertura, aperture e livelli.

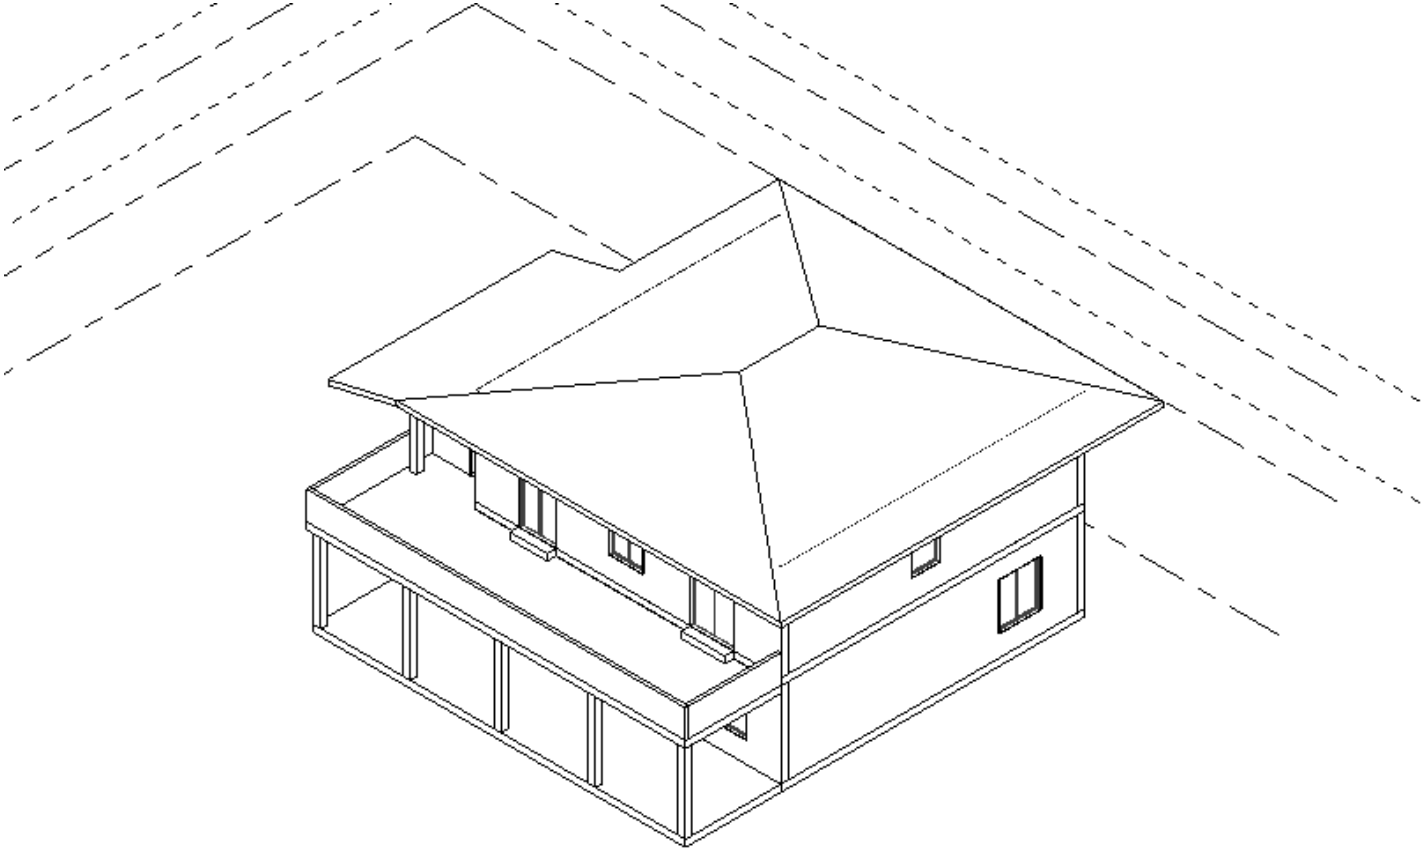

Andrea Giaquinto | Disegnatore CAD/BIM | andreagiaquinto.it

IFC / AMBIENTE BIM

Il modello viene scambiato e consultato in software compatibili con IFC, secondo le esigenze del progetto.

AMBITO DEL LAVORO

Ricostruzione delle geometrie dai documenti disponibili. Le parti non definite dalle quote richiedono verifica.

VISTA DEL MODELLO IN REVIT

Layer, colori, stili di testo e quota, cartigli e altri standard grafici possono derivare dal professionista o dal file sorgente. Sono indicativi e adattabili allo standard richiesto.

Riproduzione e diffusione vietate senza autorizzazione. andreagiaquinto.it

B


Dalla nuvola di punti al CAD

Il rilievo viene sezionato, letto e interpretato per ottenere una planimetria coerente e modificabile.

01 Lettura della sezione del rilievo

02 Interpretazione di muri e aperture

03 Restituzione e controllo in CAD

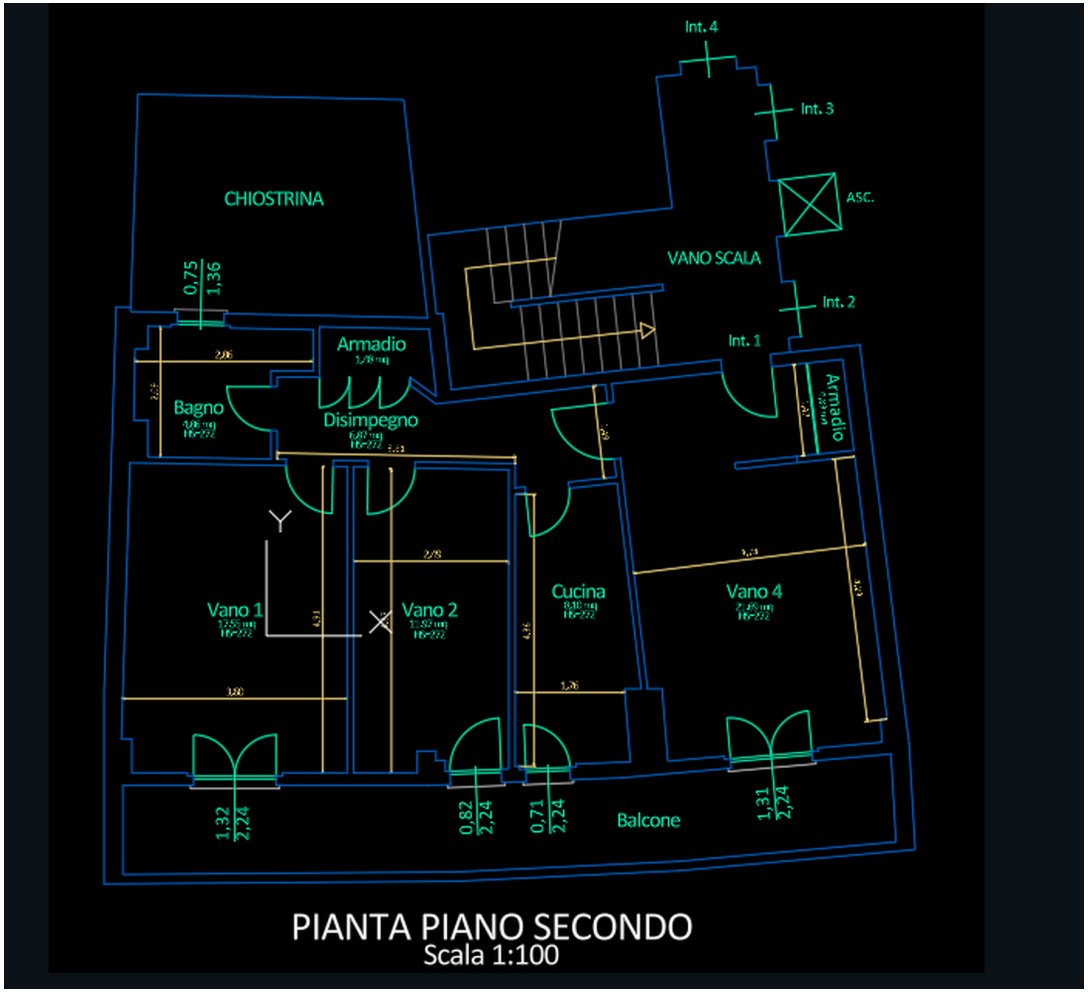

Riproduzione e diffusione vietate senza autorizzazione. andreagiaquinto.it


Dal dato misurato al disegno.

La sezione della nuvola e la restituzione CAD sono mostrate separatamente, per rendere leggibile il passaggio.

ELABORATO DI PARTENZA / NUVOLA



ELABORATO OTTENUTO / PLANIMETRIA

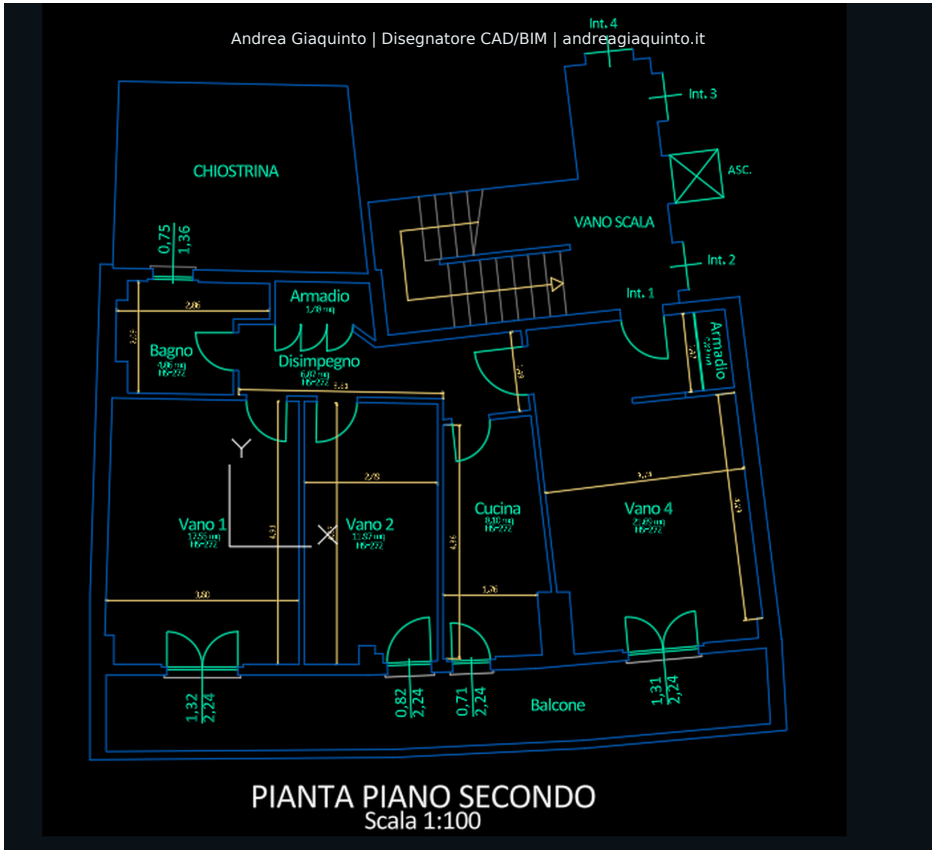


Il lavoro comprende lettura delle discontinuità, riconoscimento delle aperture e controllo delle connessioni geometriche.

Layer, colori, stili di testo e quota, cartigli e altri standard grafici possono derivare dal professionista o dal file sorgente. Sono indicativi e adattabili allo standard richiesto.

Riproduzione e diffusione vietate senza autorizzazione. andreagiaquinto.it

Geometrie organizzate, lettura pulita.

La planimetria ricostruisce perimetri, partizioni e collegamenti sulla base delle evidenze disponibili nel rilievo.

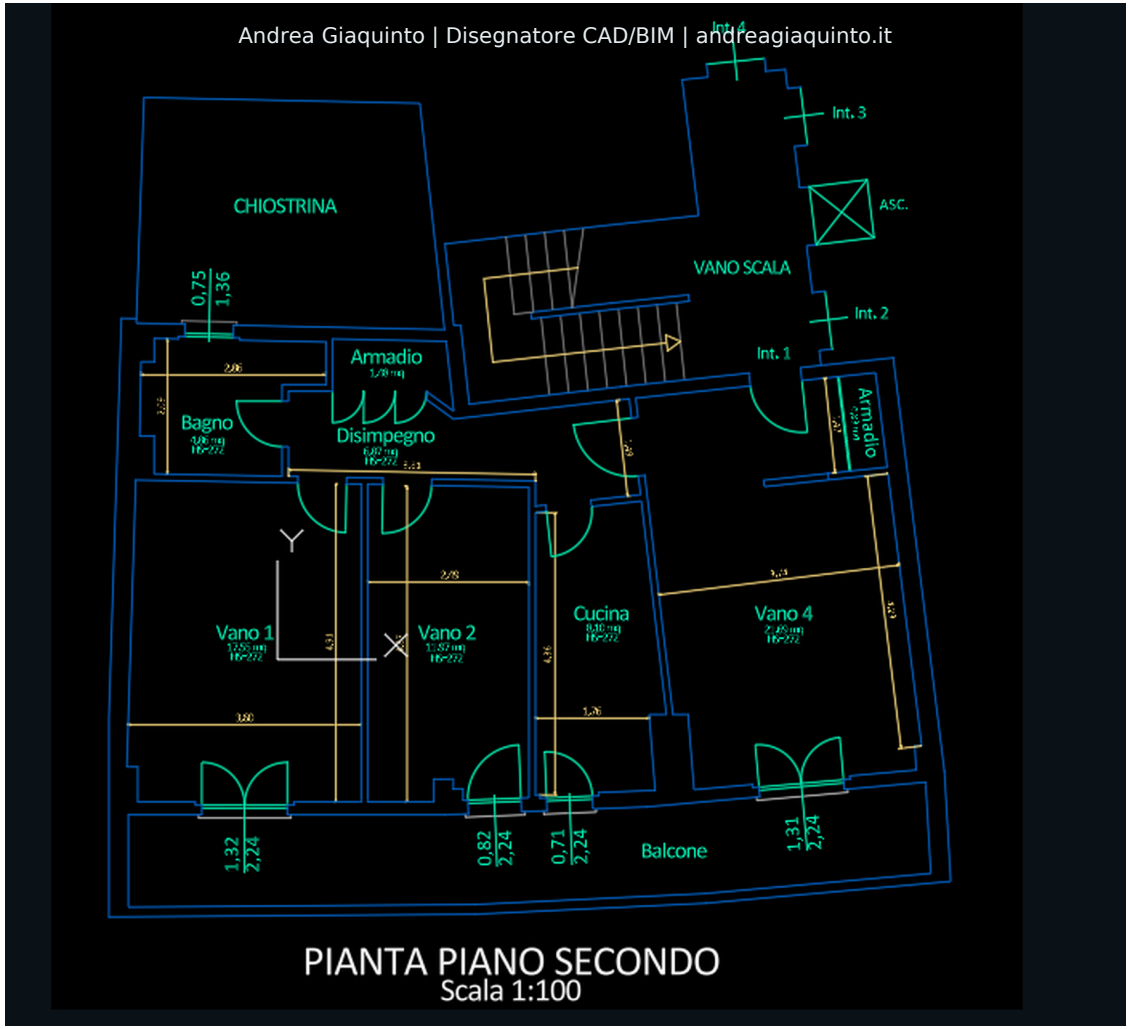

LETTURA E INTERPRETAZIONE

Distinguere muri, porte, finestre, vano scala e altri elementi dalle tracce del rilievo.

CONTROLLO DELLE GEOMETRIE

Verificare spessori, allineamenti e connessioni. Foto, planimetrie e misure integrative aiutano a risolvere le incertezze.

DWG / DXF / TAVOLE PDF

Layer, colori, stili di testo e quota, cartigli e altri standard grafici possono derivare dal professionista o dal file sorgente. Sono indicativi e adattabili allo standard richiesto.

Riproduzione e diffusione vietate senza autorizzazione. andreagiaquinto.it

C

Planimetrie commerciali

Spazi leggibili, arredi coordinati e una presentazione immediata delle possibilità abitative.

01 Lettura della distribuzione

02 Proposte di arredo e materiali

03 Viste 2D e 3D coordinate



Riproduzione e diffusione vietate senza autorizzazione. andreagiaquinto.it

Una casa, più modi di viverla.

Proposte di rappresentazione e arredo: la pianta chiarisce gli ambienti, la vista 3D ne rende percepibili volumi e relazioni.

LETTURA IN PIANTA



Andrea Giaquinto | Disegnatore CAD/BIM | andreagiaquinto.it

METODO

Distribuzione, arredi e finiture organizzati per rendere riconoscibili funzioni e collegamenti.

ELABORATO OTTENUTO / VISTA 3D



Andrea Giaquinto | Disegnatore CAD/BIM | andreagiaquinto.it

Layer, colori, stili di testo e quota, cartigli e altri standard grafici possono derivare dal professionista o dal file sorgente. Sono indicativi e adattabili allo standard richiesto.

Riproduzione e diffusione vietate senza autorizzazione. andreagiaquinto.it

Spazi compatti, lettura immediata.

Proposte di rappresentazione e arredo: la pianta chiarisce gli ambienti, la vista 3D ne rende percepibili volumi e relazioni.

LETTURA IN PIANTA



Andrea Giaquinto | Disegnatore CAD/BIM | andreagiaquinto.it

METODO

Distribuzione, arredi e finiture organizzati per rendere riconoscibili funzioni e collegamenti.

ELABORATO OTTENUTO / VISTA 3D



Andrea Giaquinto | Disegnatore CAD/BIM | andreagiaquinto.it

Layer, colori, stili di testo e quota, cartigli e altri standard grafici possono derivare dal professionista o dal file sorgente. Sono indicativi e adattabili allo standard richiesto.

Riproduzione e diffusione vietate senza autorizzazione. andreagiaquinto.it

Parliamo del tuo progetto.

Collaboro con professionisti, studi tecnici e clienti per trasformare documenti e rilievi in elaborati chiari, ordinati e utilizzabili.

01 / MATERIALE

Invia i documenti disponibili e descrivi l’elaborato che ti serve.

02 / CONFRONTO

Definiamo contenuti, formati, tempi e standard grafici.

03 / CONSEGNA

Il lavoro viene organizzato secondo le specifiche concordate.

Andrea Giaquinto

andrea.giaqui@gmail.com

+39 333 724 0544

andreagiaquinto.it

Richiedi un preventivo per il tuo progetto

Riproduzione e diffusione vietate senza autorizzazione. andreagiaquinto.it